



CONCEPT, NOT FOR FABRICATION

CalRig · github.com/BoujeeEnjinia1701/calrig

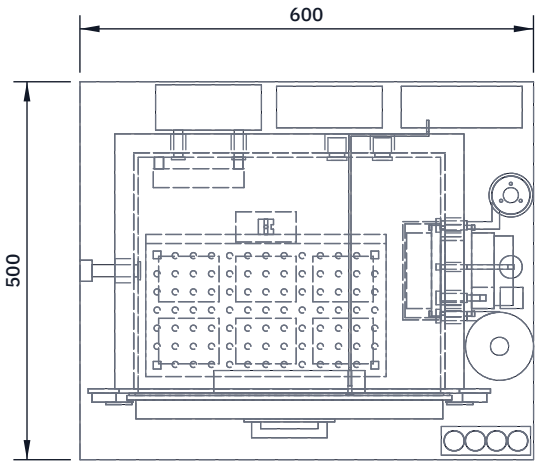


TOP VIEW

Scale 1:10; looking down (along -Z)

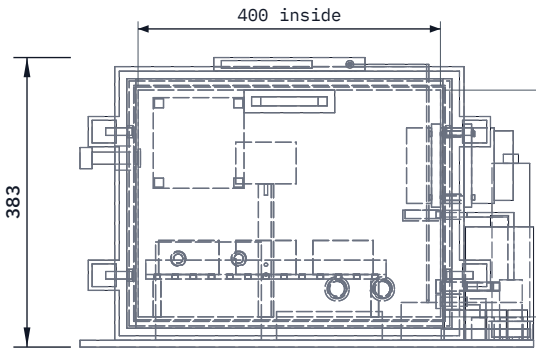

FRONT VIEW


Scale 1:10; looking at the front (along +Y)

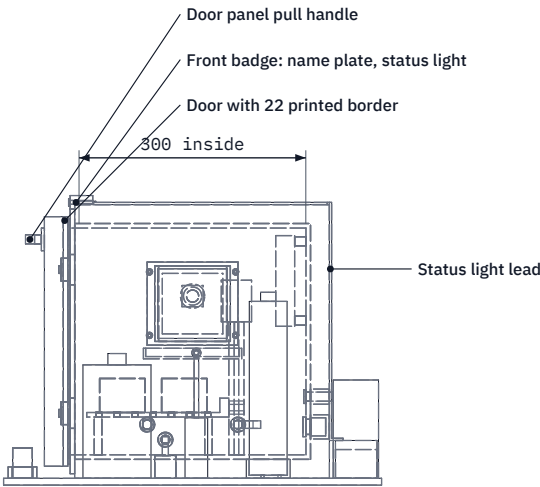

RIGHT VIEW

Scale 1:10; looking at the right side (along -X)

REV	DESCRIPTION	DATE	BY
P1	Preliminary GA for TRL 3 (from cad/src/model.py)	2026-09-25	AC
P2	Larger inner Peltier sink; mass and power notes (DDR-002)	2026-09-25	AC
P3	Layout and labels tidied	2026-09-25	AC
P4	Constructable design: frame, door, fittings, drain (DDR-003)	2026-10-01	AC
P5	Front badge, status light, door border, pull handle (DEC-001)	2026-10-02	AC

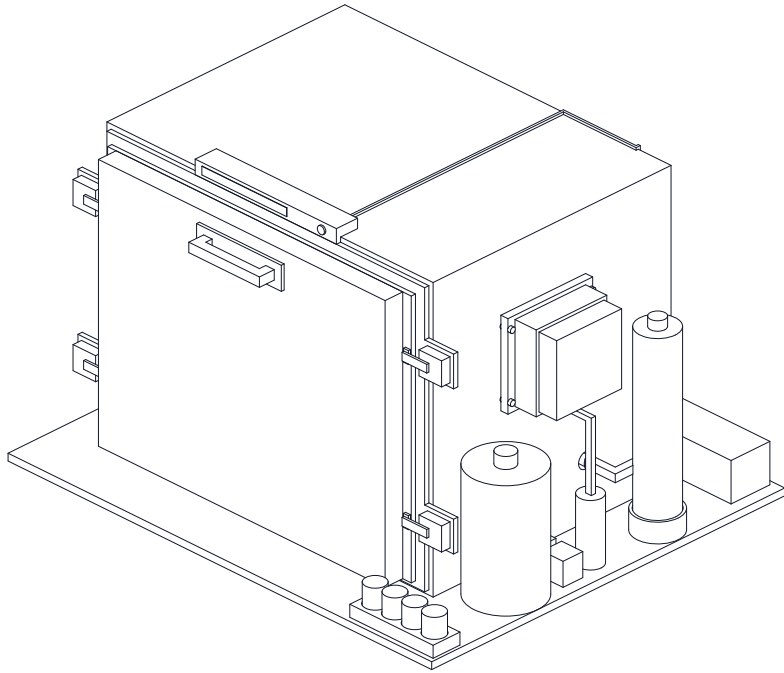

ISOMETRIC VIEW

Not to scale; door panel fitted; seen from the front right and above, about 30 deg elevation

MAIN DIMENSIONS AND INTERFACES (MM)

Chamber 400 x 300 x 300 inside (36 L), 6 acrylic
XPS jacket 25 on all faces but the door; removable door panel
Six bays 90 x 70, 244 clear above the tray (R10)
Peltier opening 90 x 100 in the +X wall; inner sink 45 x 120 x 110
Door 430 x 330 on a welded front frame, gasket, four latches
Door border 22 printed; door panel with pull handle
Front badge 200 x 30 on the top: name plate, status light
Large heads 192 x 70 in two bays, 192 x 152 in four (R10)
Bulkheads: 3 x 12 (+X), 2 x 12 to HEPA, drain 6; aerosol 16 (-X)
Base 600 x 500 x 9 plywood; overall height 383
Mass about 13.9 kg; 12 V, 90 W peak (CLR-CAL-001)
Third-angle; front view from -Y (door side)

CALRIG

github.com/BoujeeEnjinia1701/calrig

General arrangement

DRAWING NO. CLR-DWG-001			REV P5	SHEET 1 of 1	SIZE ANSI B
SCALE 1:10	UNITS mm	PROJECTION 	DATE 2026-10-02	DRAWN Amish Chadha	

MATERIAL / NOTES
Cast acrylic, XPS, plywood; bought-in parts per bom/bom.csv. PRELIMINARY, NOT FOR FABRICATION